Rochecorbon

PLU

PLAN LOCAL D'URBANISME

4.1.b PLAN DU RÉSEAU D'ALIMENTATION EN EAU POTABLE

Approbation du PLU
Vu pour être annexé à la délibération
du Conseil Métropolitain du 25 novembre 2019

Rochecorbon

Département d'Indre et Loire

Tours métropole Val de Loire

atu.
Agence d'Urbanisme de l'Agglomération de Tours
3 cour du 56, avenue Marcel Dassault
BP 603 - 37206 Tours cedex 3
Téléphone : 02 47 71 70 70
Télécopie : 02 47 71 97 35
Courriel : atu@atu37.fr
www.atu37.fr

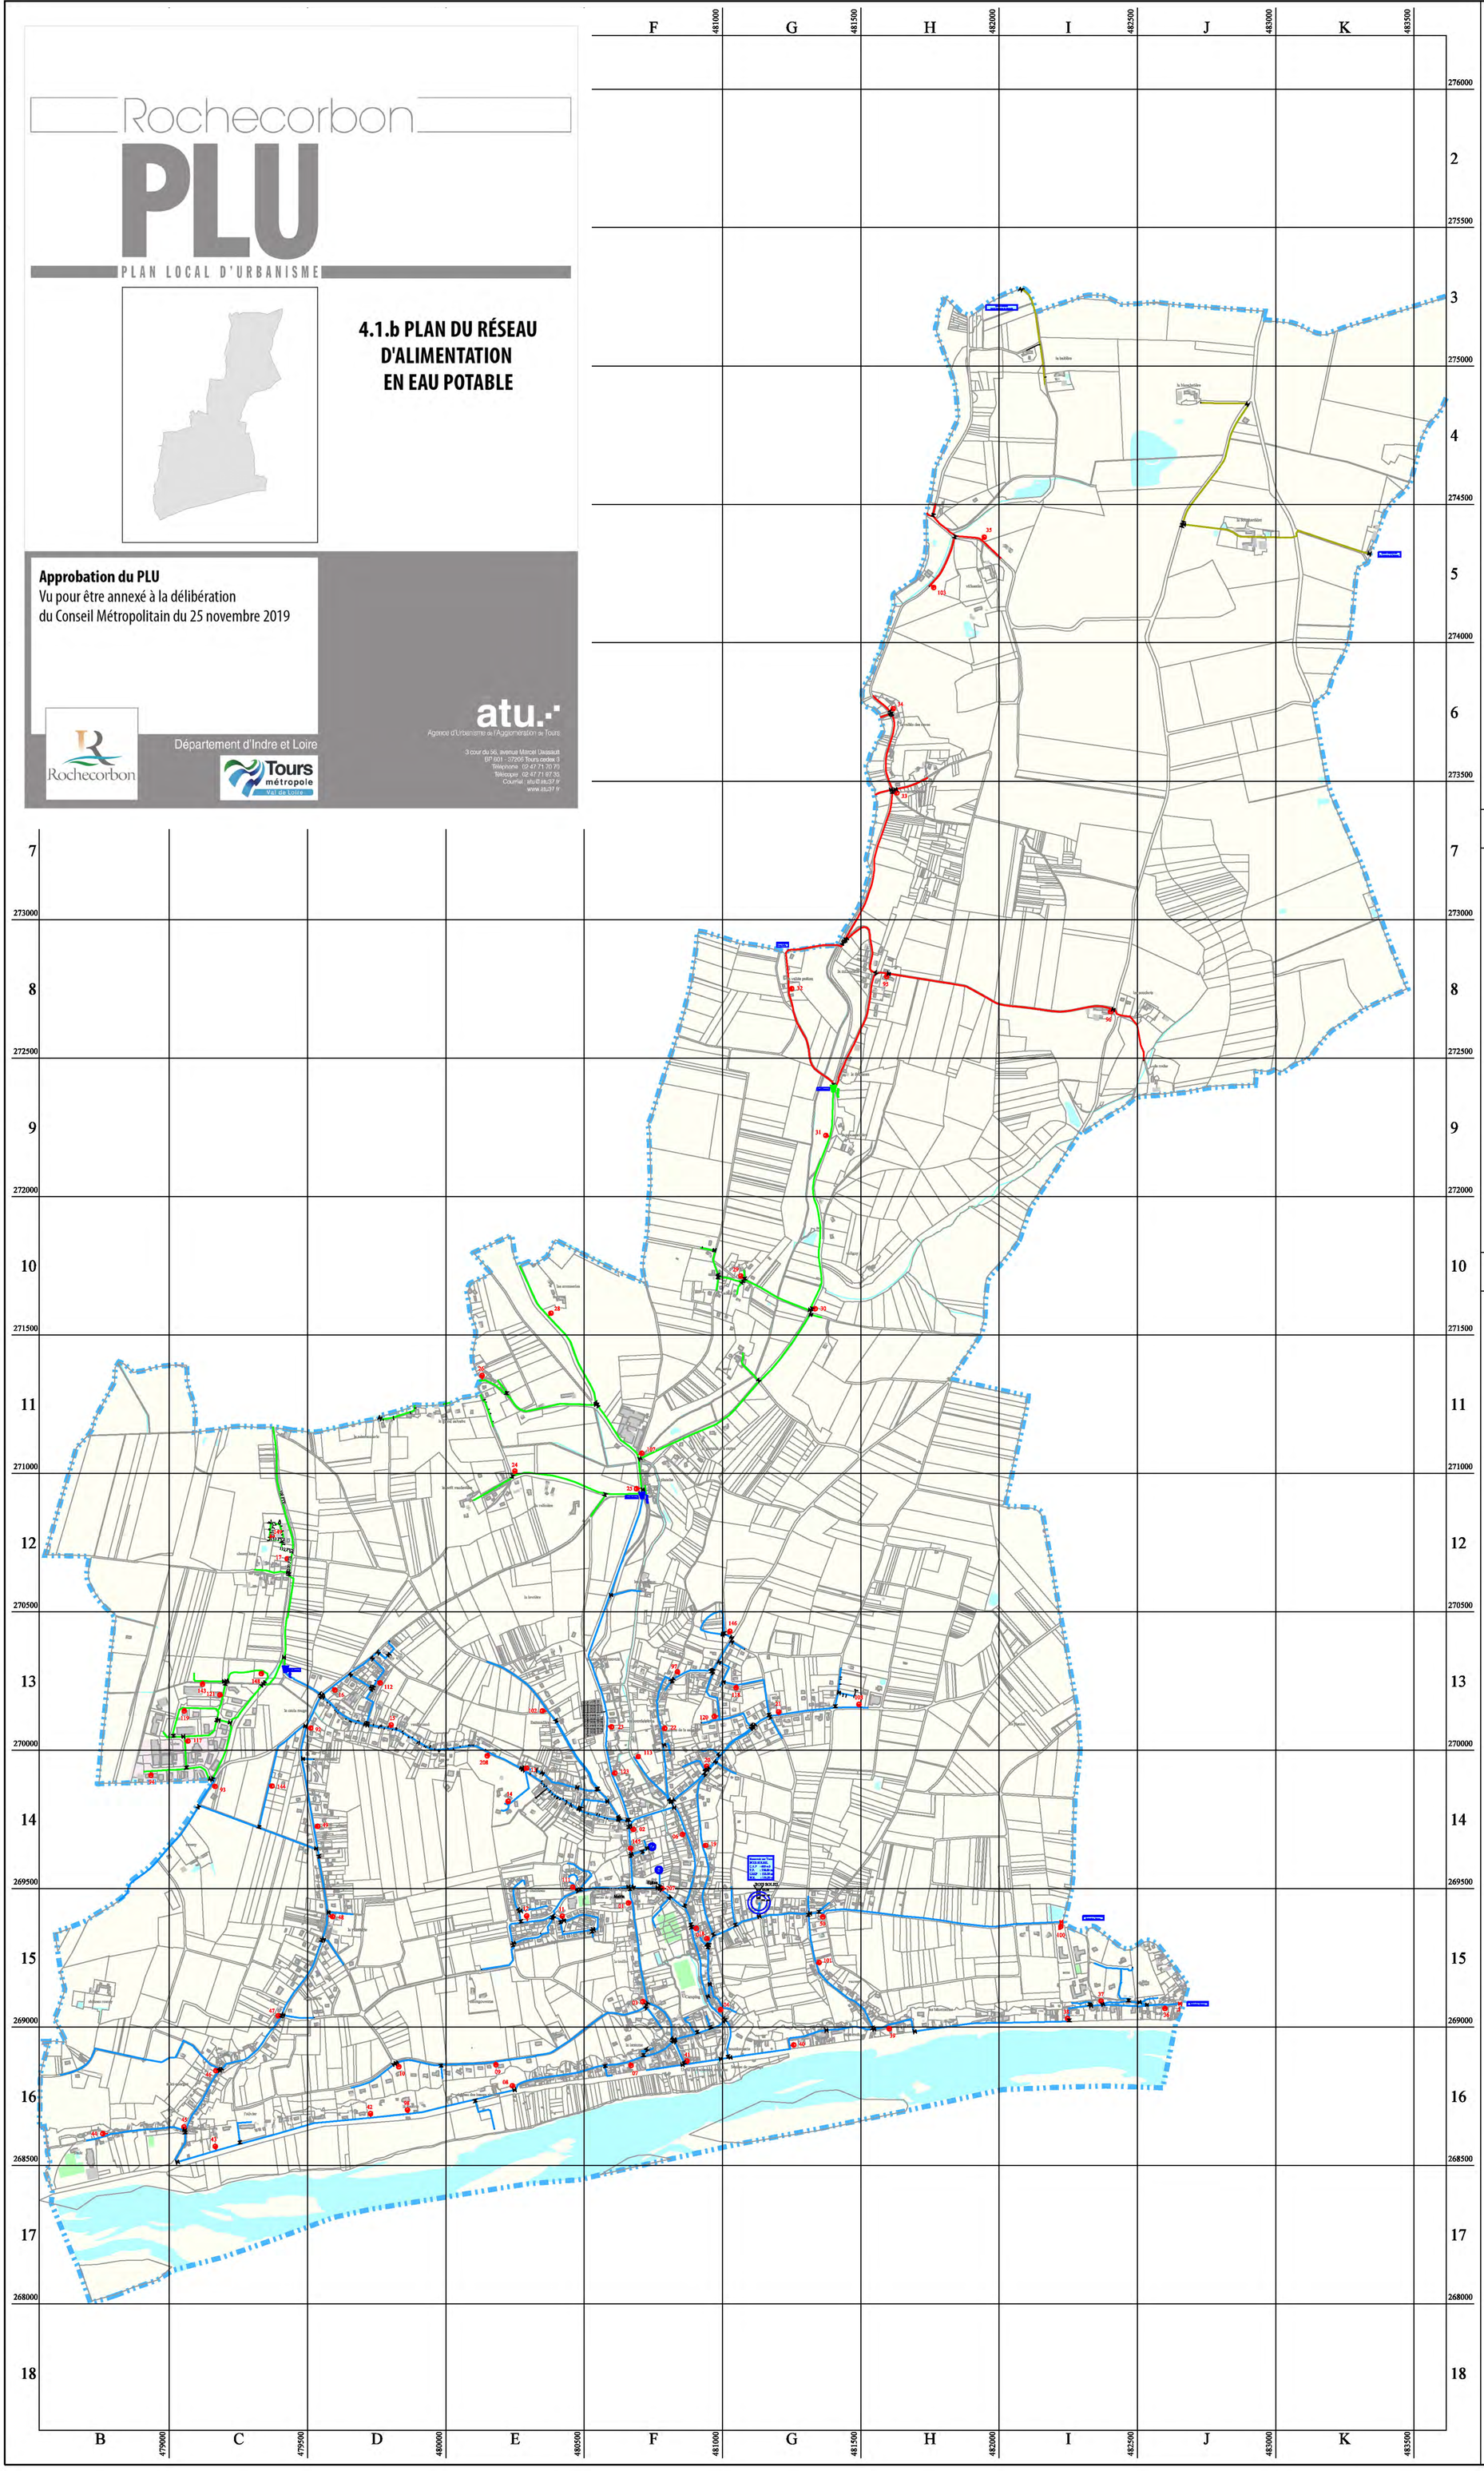

D0134 SIAEP ROCHECORBON PARCAY MESLAY

ROCHECORBON

DEPARTEMENT DE L'INDRE ET LOIRE (37)

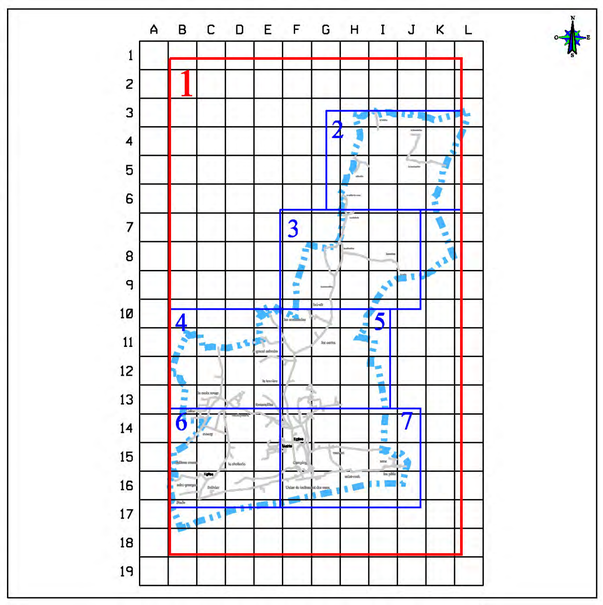

PLAN DU RESEAU EAU POTABLE

PLANCHE N° : 1 / 7

VEOLIA	CENTRE BEAUCE CHER ET LOIRE N° 3 RUE CUGNOT 37305 JOUE LES TOURS cedex 02 47 67 74 44 02 47 53 03 50	DESSINE PAR : M. NERON	VERIFIE PAR : SITE
		DATE D'IMPRESSION : 05/01/2017	ECHELLE : 1/10000

REFERENCE PLAN : \D0134-37203-AEP

FDP BD TOPO

LEGENDE

RESEAUX D'ADDUCTION D'EAU

ELEVATION 1	BRUTE
ELEVATION 2	REFOULEMENT
ELEVATION 3	RESERVOIR
ELEVATION 4	FEEDER
ELEVATION 5	PRIVES
ELEVATION 6	AUTRES
ELEVATION 7	
ELEVATION 8	

BOUCHE INCENDIE	POTEAU INCENDIE	PUITS / FORAGE
CAPTAGE	STATION DE REPRISE	STATION DE TRAITEMENT
VANNE	VANNE ELECTRIQUE	VANNE QUART DE TOUR
REGULATEUR DEBIT	REGULATEUR AMONT	POSTE DE RECHLORATION
RESERVOIR AU SOL	RESERVOIR SUR TOUR	COMPTEUR
CAPTEUR DE PRESSION	CLAPET	DECHARGE
ANODE REACTIVE	DEBITMETRE	RACCORD
PROTECTION CATHODIQUE SOUTIRAGE	PRISE DE POTENTIEL	JOINT ISOLANT
BOUCHE DE LAVAGE	BALLON	BORNE FONTAINE
CHEMINEE	CONE	CONNEXION
VENTOUSE	SOUPAPE	BRANCHEMENT
ABONNE SENSIBLE	PHOTO	CAMERA
TEXTE	DESSIN	

INDEX DES RUES

BASSES RIVIERES (Rue des)	5 6 7	E16 F16
BEAUREGARD (Rue de)	5 7	B16 C16
BEL AIR (Lieu-dit)	4 7	G10 F10
BELLEVUE (Rue de)	6 7	F14
BOIS SOLEIL (Rue du)	6 7	G15 G14
BOURDAISIERES (Rue des)	4 6 7	F14 F13 G13
BOURDONNERIE (Rue de la)	5 6 7	D16 E16 F16 F15
BUTTE (Chemin de la)	6 7	F16 F15
CALVAIRE (Rue du)	3 7	C11 D11 E11
CARTES AU C8 (Chemin des)	4 7	F11 G11 G10
CHALUTEAU (Rue du)	5 6 7	E15 E14 F14
CHAMBOISSIER (Rue Pierre)	5 7	E15 E14
CHANTECLERC (Place)	5 6 7	E15 E14
CHAPELLES (Rue des)	6 7	G15 H15 I15
CHATENAY (Allee)	3 5 7	C14 C13
CHATENAY (Allée de)	5 7	C14 C13
CHATENAY (Rue de)	5 7	B14 C14 C13
CLOS DU PINS (Allee du)	4 7	F13
CLOS MARGOT (Allée)	4 6 7	G13 G14
CLOUETS (Rue des)	6 7	F15 F14 G15 G16
COMPAGNONS (Rue des)	3 5 7	B13 C13
CROIX ROUGE (Rue de la)	3 7	D13
DORERIE (Rue de la)	3 7	E11 E10
EGLISE (Rue de l')	6 7	F15
FONTENAILLES (Rue de)	3 5 6 7	F14 E14 E13
FONTENELLES (Rue des)	4 6 7	F14 F13 E13 F12
GRANDE COUR (Chemin de la)	6 7	F14 G14
HAUTES BOURDAISIERES (Allee des)	4 7	F13 G13
HAUTES GATINIERES (Rue des)	6 7	F15 F14
HAUTS CLOUETS (Sentier des)	6 7	G15 F15
HAUTS PELUS (Sentiers des)	6 7	F14 F13
HUNXE (Allée de)	3 7	C13
LA RABATERIE (lieu-dit)	2 7	H6
LA ROCHE DENIAU (Lieu-dit)	1 7	H5
LA VALINIERE (lieu-dit)	3 7	E12
LA VALLEE DES CAVES (lieu-dit)	1 7	H6
LA VAUDANERIE (lieu-dit)	3 7	E12
LAGARDE-POUAN (Rue)	5 7	E15
LEBLED (Rue du Docteur)	6 7	F16 F15 F14
LES MONTEAUX (lieu-dit)	4 7	F13 F12
LES PLANCHES (Lieu-dit)	4 7	F12 F11
MARECHAUX (Allée des)	6 7	F14
MATHIEU (Rue du Commandant)	5 6 7	E15 D15 F15 F14
MESSAGERS (Rue des)	3 5 7	C13
MONTAURAN (Rue de)	6 7	I15 J15
MOSNY (Chemin)	5 7	D15 C15
MOULIN DE TOUVOIE (lieu-dit)	4 7	F13
MOULIN (Rue du)	6 7	F16 F15 G15
N° 129 (c.d)	3 5 7	C14 C13 C12 C11
PATIS (Rue des)	6 7	J15
PATIS (Sentier des)	6 7	J15 I15
PELUS (Rue des)	4 6 7	G13 G14 F14
PELUS (Sentier des)	6 7	F14 F13
PEU BOULIN (Sentier du)	6 7	F15
PEU BOULIN (Rue du)	6 7	F15 G15
POIRIER LA BELLE (lieu-dit)	4 7	H13
RABASSOUS (Allée des)	4 7	G13 F13
RAIMBAUDERIE (Rue de la)	3 7	D11 E11
R.N° 152 (route)	5 6 7	J15 I15 H15 H16 G16 F16 E16 D16 C16 C17 B17
SAINT GEORGES (Ruette)	5 7	C16
SAINT-GEORGES (Rue de)	3 5 7	D13 C13 C14 D14 D15 C15 C16
SAINT-ROCH (Rue)	6 7	G16 G15 H16 H15
SENS (Rue de)	6 7	I15 J15
TREILLE (Rue de la)	5 6 7	E15 F15
TUVOIE (Cheminde)	4 7	F13
VALINIERE (Rue de la)	3 7	D13 D12
VALLEES (Impasse sous les)	4 6 7	F14 F13
VAUFOYNARD (Rue de)	3 5 6 7	F14 E14 E13 D13
VAUVERT (Rue de)	6 7	G14 G15 H15 H16
VIGNES (Rue des)	4 7	G13
VILLESETIER (Lieu-dit)	1 7	I5
VINETTERIE (Chemin de la)	5 7	D15
8 MAI 1945 (Place du)	6 7	F15